
SUPPLY SCOPE (distributor quantities issue, no material prices): Nudura 6in XR35 external walls, GF + FF to the wall plate, ICF on the slab, plus the two front gables - pre-cut by BuildEase, stock forms and accessories by the distributor. Everything else (slab, floors, roof, internal walls, chimney, windows, finishes) is shown or assumed in good faith only and must be checked by the relevant professional; the engineer to design the walls.

QUOTATION - NOT FOR CONSTRUCTION

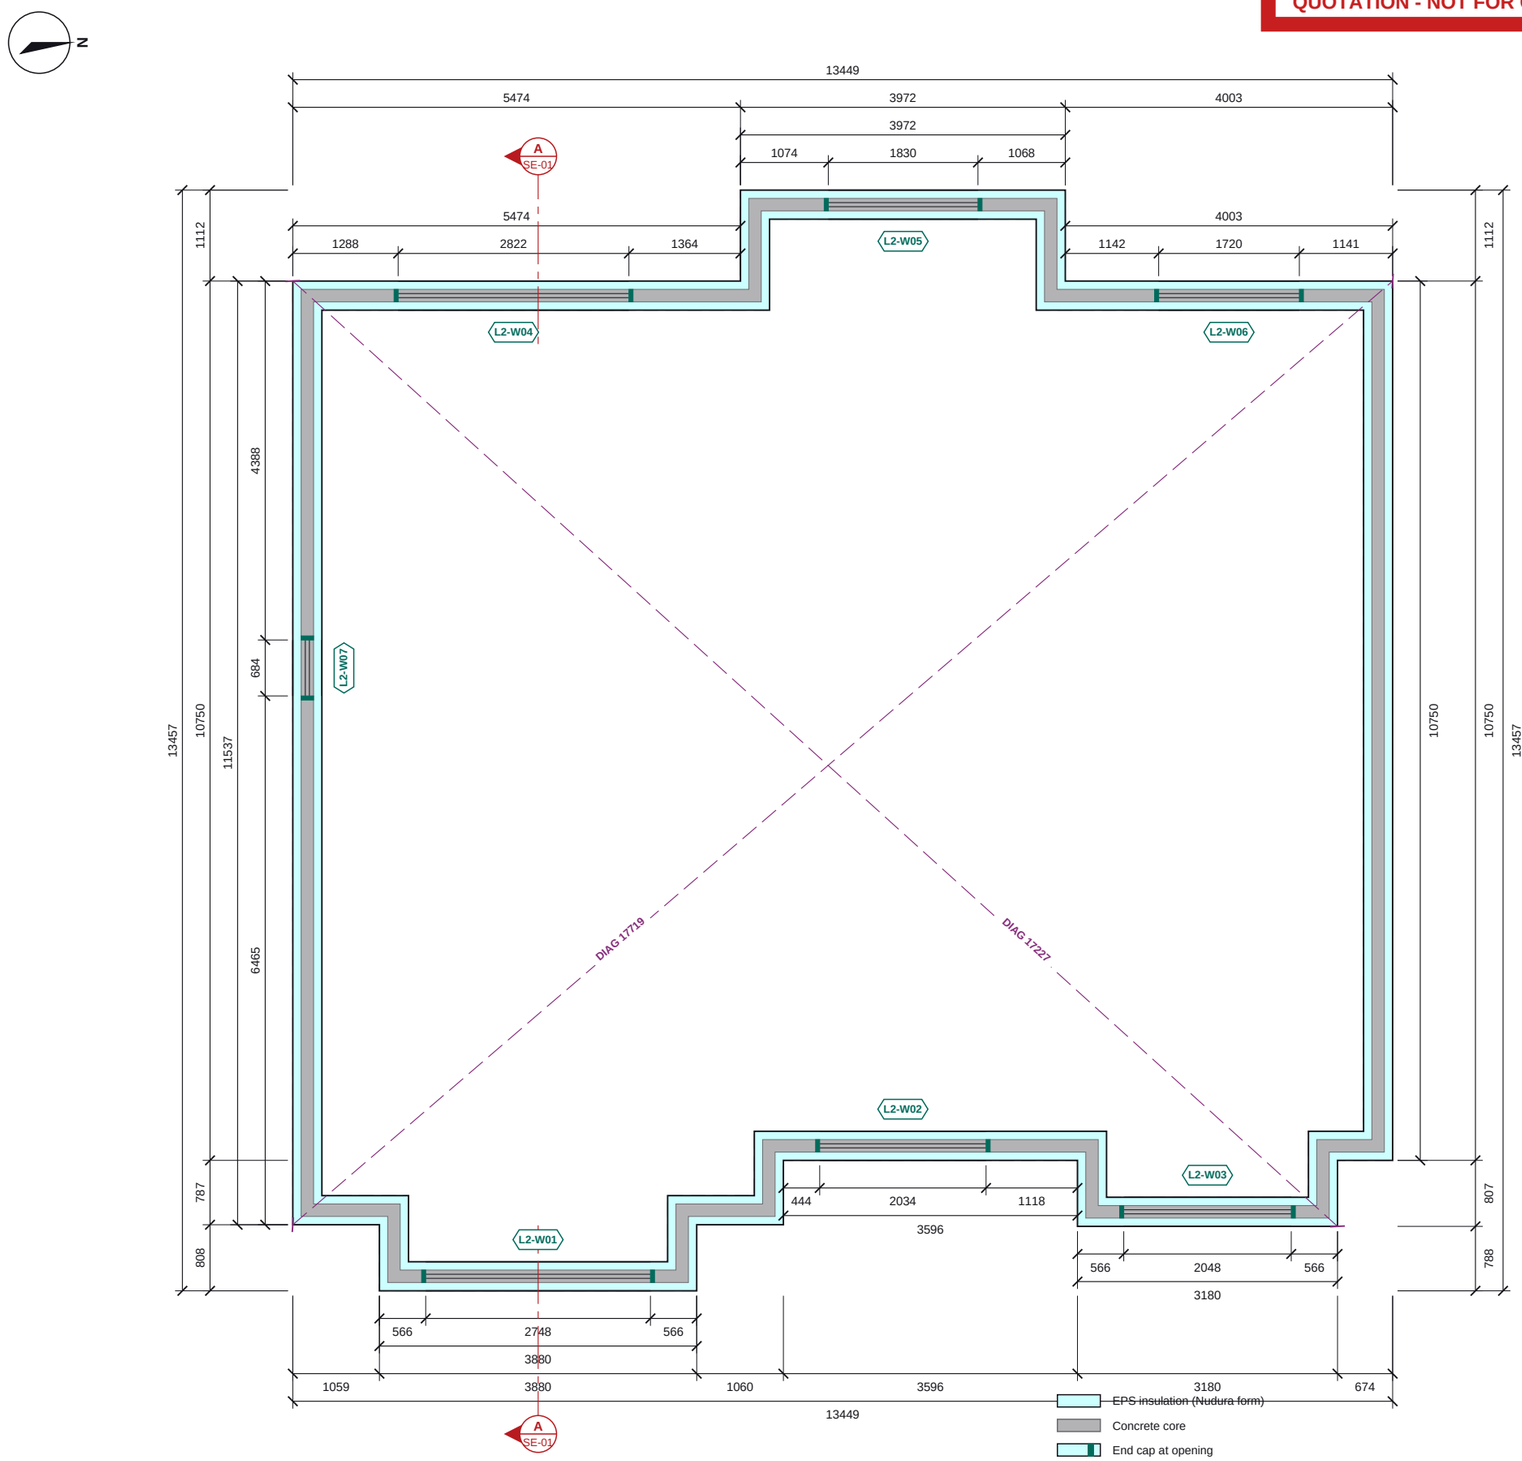

FIRST FLOOR (TO PLATE, 12 CRS) ICF PLAN

Scale 1:75 @ A3 | Plan cut at +3643

0 1 2 3 4m

FIRST FLOOR (TO PLATE, 12 CRS) ICF SCHEDULES

OPENING SCHEDULE

Ref	Width	Height	Sill	Head	Lintel
L2-W01	2748	1370	+3830	+5200	-
L2-W02	2034	1370	+3830	+5200	-
L2-W03	2048	1370	+3830	+5200	-
L2-W04	2822	1440	+3710	+5150	-
L2-W05	1830	1420	+3730	+5150	-
L2-W06	1720	1440	+3710	+5150	-
L2-W07	684	1400	+3700	+5100	-

Structural openings in the ICF; sill and head above GF FFL.

NOTES

1. ICF: Nudura 6" XR35, 101.6 EPS + 152.4 core + 101.6 EPS = 355.6. Dimensions to the ICF faces.
2. Levels above GF FFL. Sill / head = structural opening in the ICF.
3. No structural design issued. 6in XR35 (152 core) external walls from the architect's preliminary plans; reinforcement, lintels over the wide bay / door openings, the oversailing left gable and the mix for the engineer.
4. Lintel (L-n) and steel (B-n, C-1) marks from rev -, which takes precedence.
5. Masonry walls shown for context.
6. Datum: 0 = GF FFL / top of slab (ICF starts on the slab, no footing blocks).
7. From Offset Architects 9172-SK10 Plot 1 Plans and Elevations (PRELIMINARY, July 2026).

REVISIONS

REV	DATE	DESCRIPTION
-	02.11.26	Quotation issue

Nudura™ BuildEase

CLIENT	PROJECT
ICF Supplies Ltd (distributor) - Tom Barrett	Plot 1, The Rectory, Bates Hill, Ightham TN15 9BG

DRAWING TITLE

FIRST FLOOR ICF GENERAL ARRANGEMENT

ICF walls, openings, lintels, steel over and engineer's notes

SCALE	SIZE	DATE
1:75	A3	02.11.26
DRAWN	CHECKED	APPROVED
TS		

STATUS	DRAWING No.	REV
QUOTATION	ES26-075-GA-02	-

Do not scale. All dimensions in millimetres, levels in metres from GF FFL. Check all dimensions on site.