
SUPPLY SCOPE (distributor quantities issue, no material prices): Nudura 6in XR35 external walls, GF + FF to the wall plate, ICF on the slab, plus the front gables - pre-cut by BuildEase, stock forms and accessories by the distributor. The slab, floors, steels, stairs, roof, partitions, windows, chimney and porch are DESIGN ASSUMPTIONS drawn in good faith for coordination only (England - Approved Documents) - engineer / specialists to design.

QUOTATION - NOT FOR CONSTRUCTION

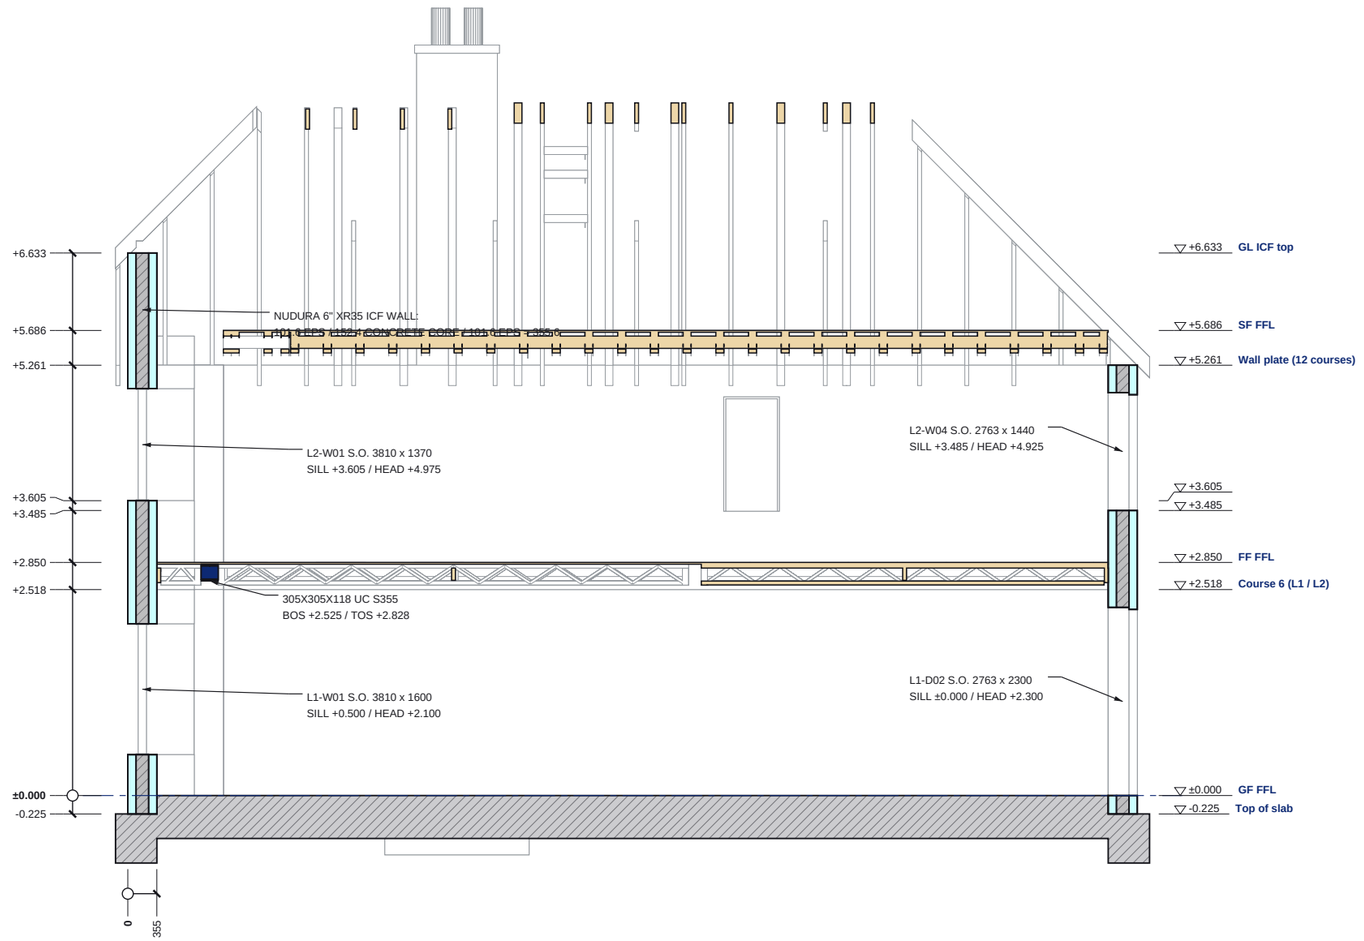

SECTION A-A

Scale 1:75 @ A3 | Looking west; levels above GF FFL

ICF EPS (cut)
ICF concrete core / RC (cut)
Steel (cut)
Insulation (PIR)
Timber (cut)
Beyond the cut (line work)

0 1 2 3 4m

SECTION A-A SCHEDULES


LEVELS ON THIS SECTION

Level	FFL
Top of slab	-0.225
GF FFL	±0.000
Course 6 (L1 / L2)	+2.518
FF FFL	+2.850
top of ICF W02	+3.485
top of ICF W16	+3.605
Wall plate (12 courses)	+5.261
SF FFL	+5.686
GL ICF top	+6.633

STEEL CUT BY THIS SECTION

Mark	Section (engineer)	BOS	TOS
-	305x305x118 UC S355	+2.525	+2.828

SECTION KEY

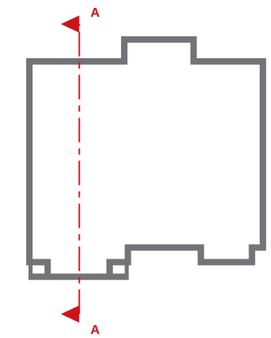

NOTES

1. Section A-A is a BuildEase ICF section (not an architect's section line). Cut elements hatched / filled; the model beyond the cut in line work.
2. Levels above GF FFL.
3. ICF: Nudura 6" XR35, 101.6 EPS + 152.4 core + 101.6 EPS = 355.6, 152.4 core + 101.6 EPS = 355.6. No structural design issued. 6in XR35 (152 core) external walls from the architect's preliminary plans; reinforcement, lintels over the wide bay / door openings, the oversailing left gable and the mix for the engineer.
4. Steel marks, BOS / TOS: rev -. See ES26-075-GA-01 / EL-01 / EL-02 in the approval drawings pack.
5. Datum: 0 = top of slab (ICF starts on the slab, no footing blocks); GF FFL = +225 (150 PIR + 75 screed inside the ICF).
6. Rev A: walls fitted to Nudura Bond (203 increments) - overall width 13,360, runs within about 100 of the drawing; architect to confirm.
7. From Offset Architects 9172-SK10 Plot 1 Plans and Elevations (PRELIMINARY, July 2026).

REVISIONS

REV	DATE	DESCRIPTION
-	02.11.26	Quotation issue
A	05.11.26	Revised to ICF Supplies review

Nudura™ BuildEase

CLIENT	PROJECT
ICF Supplies Ltd (distributor) - Tom Barrett	Plot 1, The Rectory, Bates Hill, Ightham TN15 9BG

DRAWING TITLE
SECTION A-A
ICF section with levels and build-ups

SCALE	SIZE	DATE
1:75	A3	05.11.26
DRAWN	CHECKED	APPROVED
TS		

STATUS	DRAWING No.	REV
QUOTATION	ES26-075-SE-01	A

Do not scale. All dimensions in millimetres, levels in metres from GF FFL. Check all dimensions on site.