

SUPPLY SCOPE (distributor quantities issue, no material prices): Nudura 6in XR35 external walls, GF + FF to the wall plate, ICF on the slab, plus the front gables - pre-cut by BuildEase, stock forms and accessories by the distributor. The slab, floors, steels, stairs, roof, partitions, windows, chimney and porch are DESIGN ASSUMPTIONS drawn in good faith for coordination only (England - Approved Documents) - engineer / specialists to design.

QUOTATION - NOT FOR CONSTRUCTION

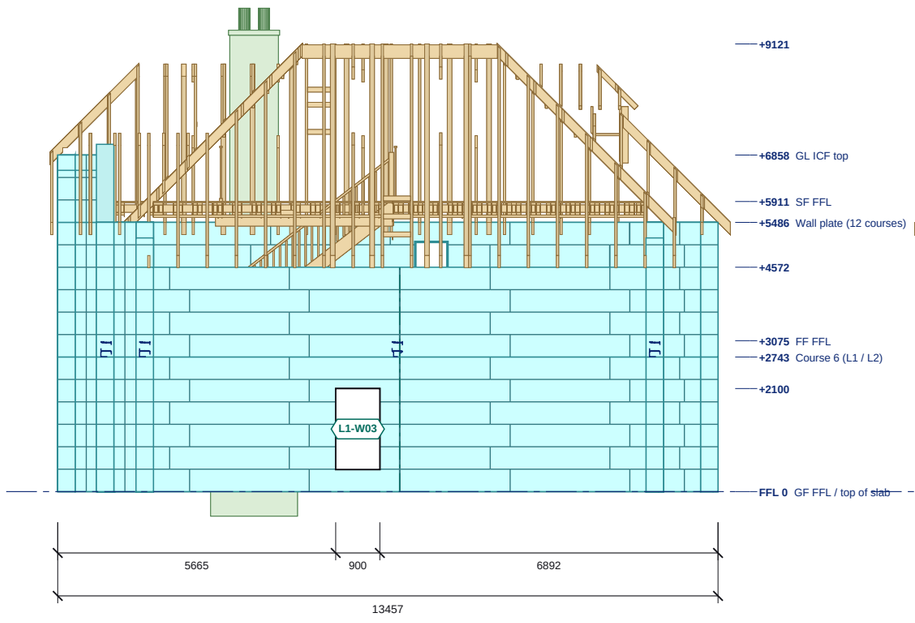

SIDE (NORTH) ELEVATION

Scale 1:125 @ A3 | Levels above GF FFL; sills and heads in the schedule

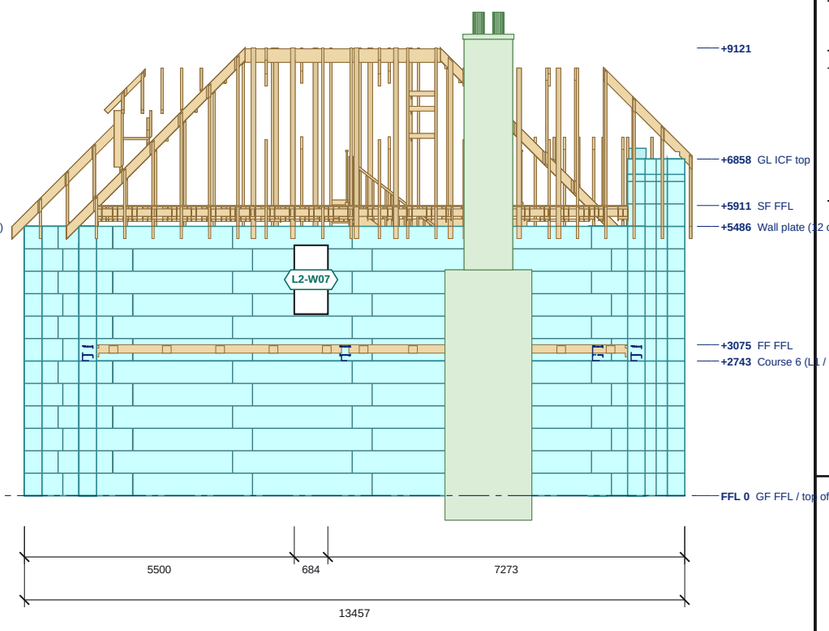

SIDE (SOUTH) ELEVATION

Scale 1:125 @ A3 | Levels above GF FFL; sills and heads in the schedule

ICF external EPS face
Block course joint
Stack joint

0 1 2 3 4 5m

ELEVATION SCHEDULES

SIDE (NORTH) ELEVATION: OPENINGS

Ref	Width	Height	Sill	Head	Lintel
L1-W03	900	1650	+450	+2100	-

Structural openings in the ICF; sill and head above GF FFL.

SIDE (SOUTH) ELEVATION: OPENINGS

Ref	Width	Height	Sill	Head	Lintel
L2-W07	684	1400	+3700	+5100	-

Structural openings in the ICF; sill and head above GF FFL.

SIDE (NORTH) ELEVATION: LEVELS

Level	FFL
GF FFL / top of slab	0
top of ICF	+2100
Course 6 (L1 / L2)	+2743
FF FFL	+3075
top of ICF	+4572
Wall plate (12 courses)	+5486
SF FFL	+5911
GL ICF top	+6858
top of roof build-up	+9121

SIDE (SOUTH) ELEVATION: LEVELS

Level	FFL
GF FFL / top of slab	0
Course 6 (L1 / L2)	+2743
FF FFL	+3075
Wall plate (12 courses)	+5486
SF FFL	+5911
GL ICF top	+6858
top of roof build-up	+9121

NOTES

1. ICF: Nudura 6" XR35, 101.6 EPS + 152.4 core + 101.6 EPS = 355.6. External EPS face shown with the block course joints, vertical block joints and stack joints as populated.
2. Levels above GF FFL. Openings are structural openings in the ICF; glazing, doors, render and finishes by others, not shown.
3. ICF walls as modelled.
4. See ES26-075-GA-01 for plan setting out, lintels and steel.
5. Datum: 0 = GF FFL / top of slab (ICF starts on the slab, no footing blocks).
6. From Offset Architects 9172-SK10 Plot 1 Plans and Elevations (PRELIMINARY, July 2026).

REVISIONS

REV	DATE	DESCRIPTION
-	02.11.26	Quotation issue

Nudura™ BuildEase

CLIENT	PROJECT
ICF Supplies Ltd (distributor) - Tom Barrett	Plot 1, The Rectory, Bates Hill, Ightham TN15 9BG

DRAWING TITLE

SIDE ELEVATIONS

ICF elevations with openings, levels and roof build-up

SCALE	SIZE	DATE
1:125	A3	02.11.26
DRAWN	CHECKED	APPROVED
TS		

STATUS	DRAWING No.	REV
QUOTATION	ES26-075-EL-02	-

Do not scale. All dimensions in millimetres, levels in metres from GF FFL. Check all dimensions on site.